APPLICABLE CODES

FLORIDA BUILDING CODE, 2023
FLORIDA BUILDING CODE EXISTING BUILDING, 2023
FLORIDA MECHANICAL CODE, 2023
FLORIDA FUEL GAS CODE, 2023
FLORIDA PLUMBING CODE, 2023 Ⓑ
FLORIDA ACCESSIBILITY CODE, 2023
FLORIDA ENERGY CONSERVATION CODE, 2023
N.F.P.A 101, LIFE SAFETY CODE FLORIDA EDITION, 2020
NATIONAL ELECTRICAL CODE, 2020

BUILDING CODE ANALYSIS

EXISTING RESTAURANT: 3937 SQFT
NEW ADDITION RESTAURANT: 1897 SQFT
EXISTING STRUCTURE: MAIN - 21' FLOOR TO CEILING
OCCUPANCY CLASSIFICATION (CHAPTER 3 FBC):
303.3 GROUP A-2 RESTAURANTS (WITH EXISTING KITCHEN)

PLAZA TENANT A (ASSEMBLY) AND B (BUSINESS)SEPARATION
(TABLE 508.4) - NON SPRINKLERED - 2 HOUR REQUIRED
TENANT AND CORRIDOR - N/A

BUILDING CONSTRUCTION TYPE (FBC 602.5 TABLE)
TYPE II-A , NON SPRINKLERED

EXIT ACCESS TRAVEL DISTANCE (TABLE 1017.2)
GROUP A NON SPRINKLERED = 200FT Ⓒ

NUMBER OF EXITS - 2 EXITS (TABLE 1006.2.1 AND 1006.2.1.1)
2 EXITS REQUIRED , OCCUPANCY LESS THAN 500

COMMON PATH OF EGRESS TRAVEL (TABLE 1006.2.1)
GROUP A = 75 FT. NON SPRINKLERED

CORRIDORS (SECTION 1020):
N/A - NO CORRIDOR IN FACILITY

A.WALL FIRE RESISTANCE RATING (TABLE 1020.1) : N/A
B.CORRIDOR WIDTH (TABLE 1020.2): N/A
C.DEAD END CORRIDORS (SECTION 1020.4): N/A

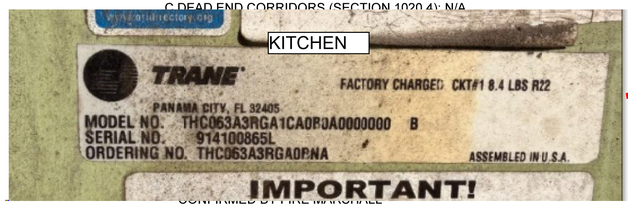

CONFIRMED BY FIRE MARSHAL

- FIRE DEPARTMENTS SHALL BE NOTIFIED PRIOR TO SHUTTING DOWN ANY FIRE PROTECTIONS SYSTEMS AND NOTIFIED AGAIN WHEN SYSTEM IS RETURNED TO NORMAL OPERATIONS

EXISTING FIRE PROTECTION SYSTEM SHALL BE MAINTAINED

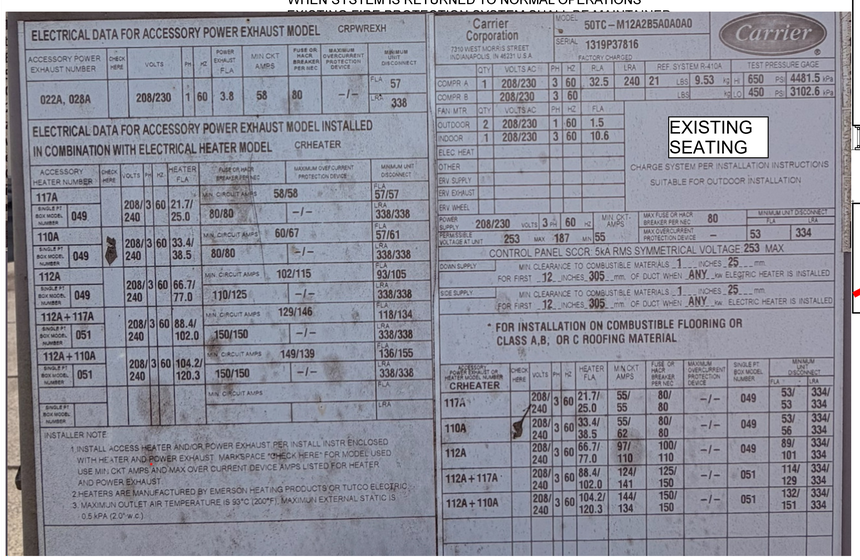

PLUMBING FIXTURE REQUIREMENTS

PLUMBING FIXTURES PER 2023 PBC PLUMBING
TABLE 403.1MINIMUM NUMBER OF REQUIRED PLUMBING FIXTURES
403.3.4 LOCATION OF TOILET FACILITIES IN MALLS
138 OCCUPANCY GROUP A BUSINESS - 69 MALE AND 69 FEMALE

CLASSIFICATION	WATER CLOSETS		LAVATORY		SERVICE SINK
ASSEMBLY RESTAURANTS,	MALE 69	FEMALE 69	MALE 69	FEMALE 69	
	1 PER 75 = 1	1 PER 75 = 1	1 PER 200 = 1	1 PER 200 = 1	1 SERVICE SINK
REQUIRED	1	1	1	1	1 SERVICE SINK
EXISTING	3	3	1	1	1 SERVICE SINK

410.4 DRINKING FOUNTAIN REQUIRED - RESTAURANTS WATER TO BE SERVED

OCCUPANT LOAD NFPA 1: TABLE 14.8.1.2

RM#	RM NAME	FUNCTION OF SPACE	OCC. LOAD FACTOR	SQFT	TOTAL
01	NEW SITTING AREA 01	ASSEMBLY LESS CONCENTRATED USE, WITHOUT FIXED SEATING	15 NET	650	44
02	NEW SITTING AREA 02	ASSEMBLY LESS CONCENTRATED USE, WITHOUT FIXED SEATING	15 NET	254	17
03	CIRCULATIONS	CIRCULATIONS	N/A	270	
04	UNISEX RESTROOM	TOILET	N/A	105	
			TOTAL OCCUPANT		61

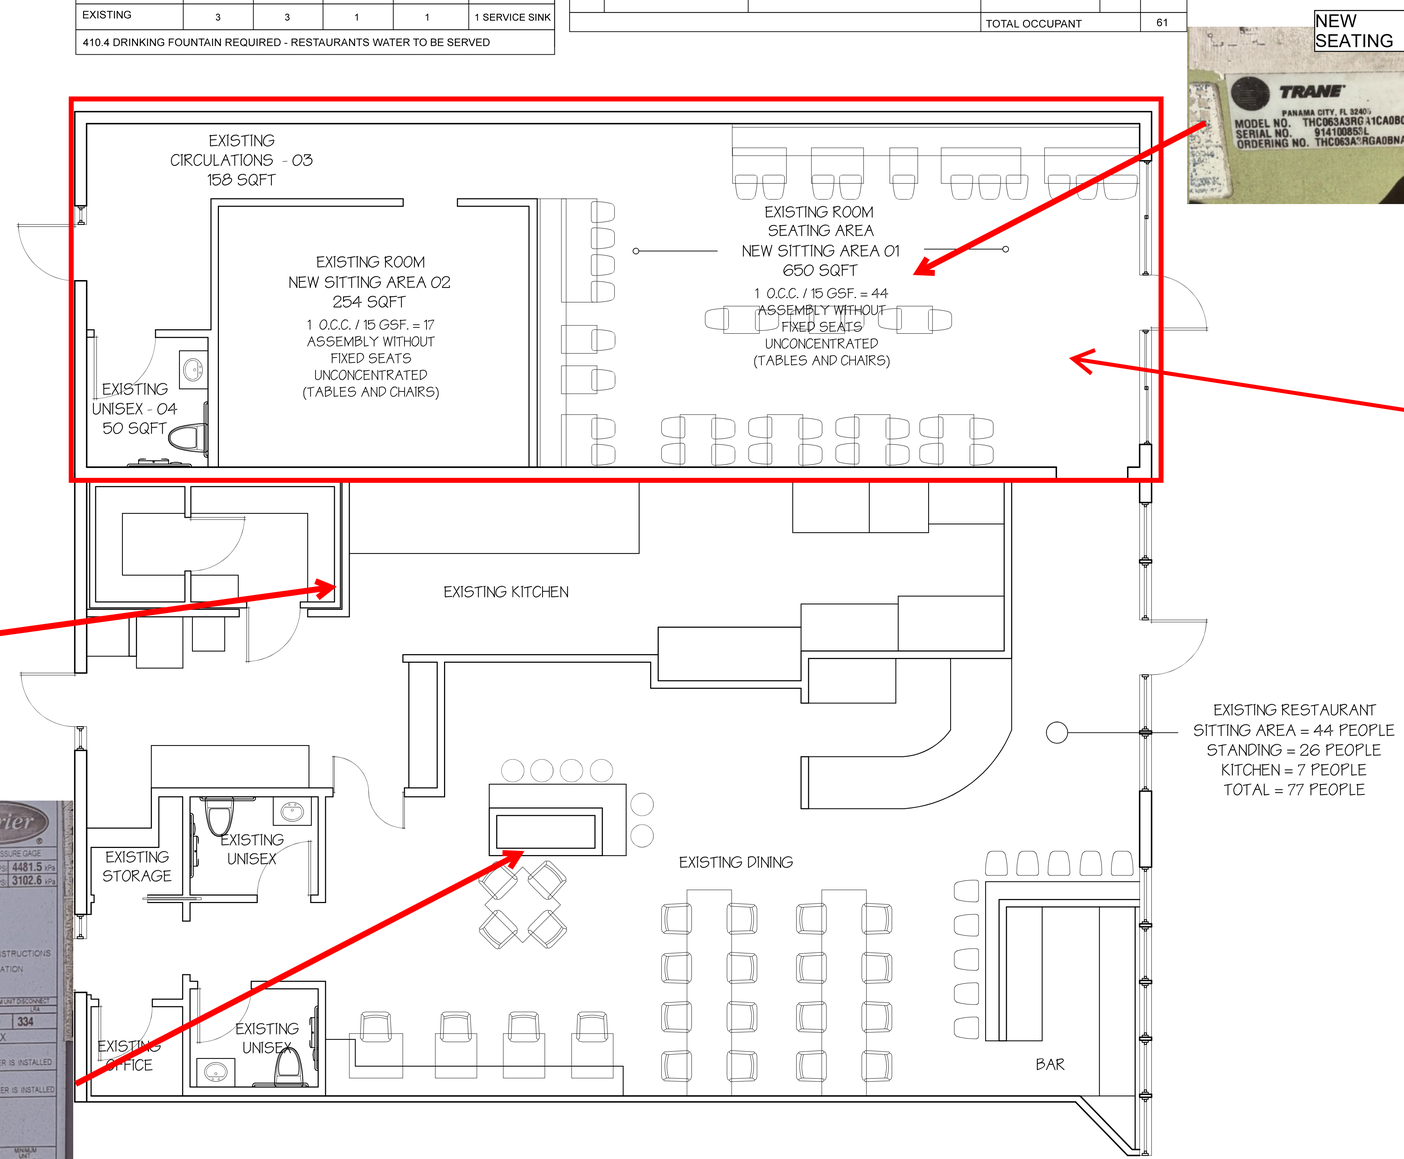

vetrano architects

MICHAEL VETRANO ARCHITECT . FL # 94957
820 MACY ST, WEST PALM BEACH, FL 33405
VETRANODESIGN.COM . 561.358.9231

© COPYRIGHT 2024 . MICHAEL VETRANO . "ALL RIGHTS RESERVED"

DATE:
12/30/2025

BLDG. DEPT.
PLAN
REVISIONS:

PROPERTY REMODEL
100 SANSBURYS WAY #108,
WEST PALM BEACH, FL 33411

MANAGED BY:MV
DRAWN BY:MV
JOB#2512216

SHEET:
A1