0F Lower Level

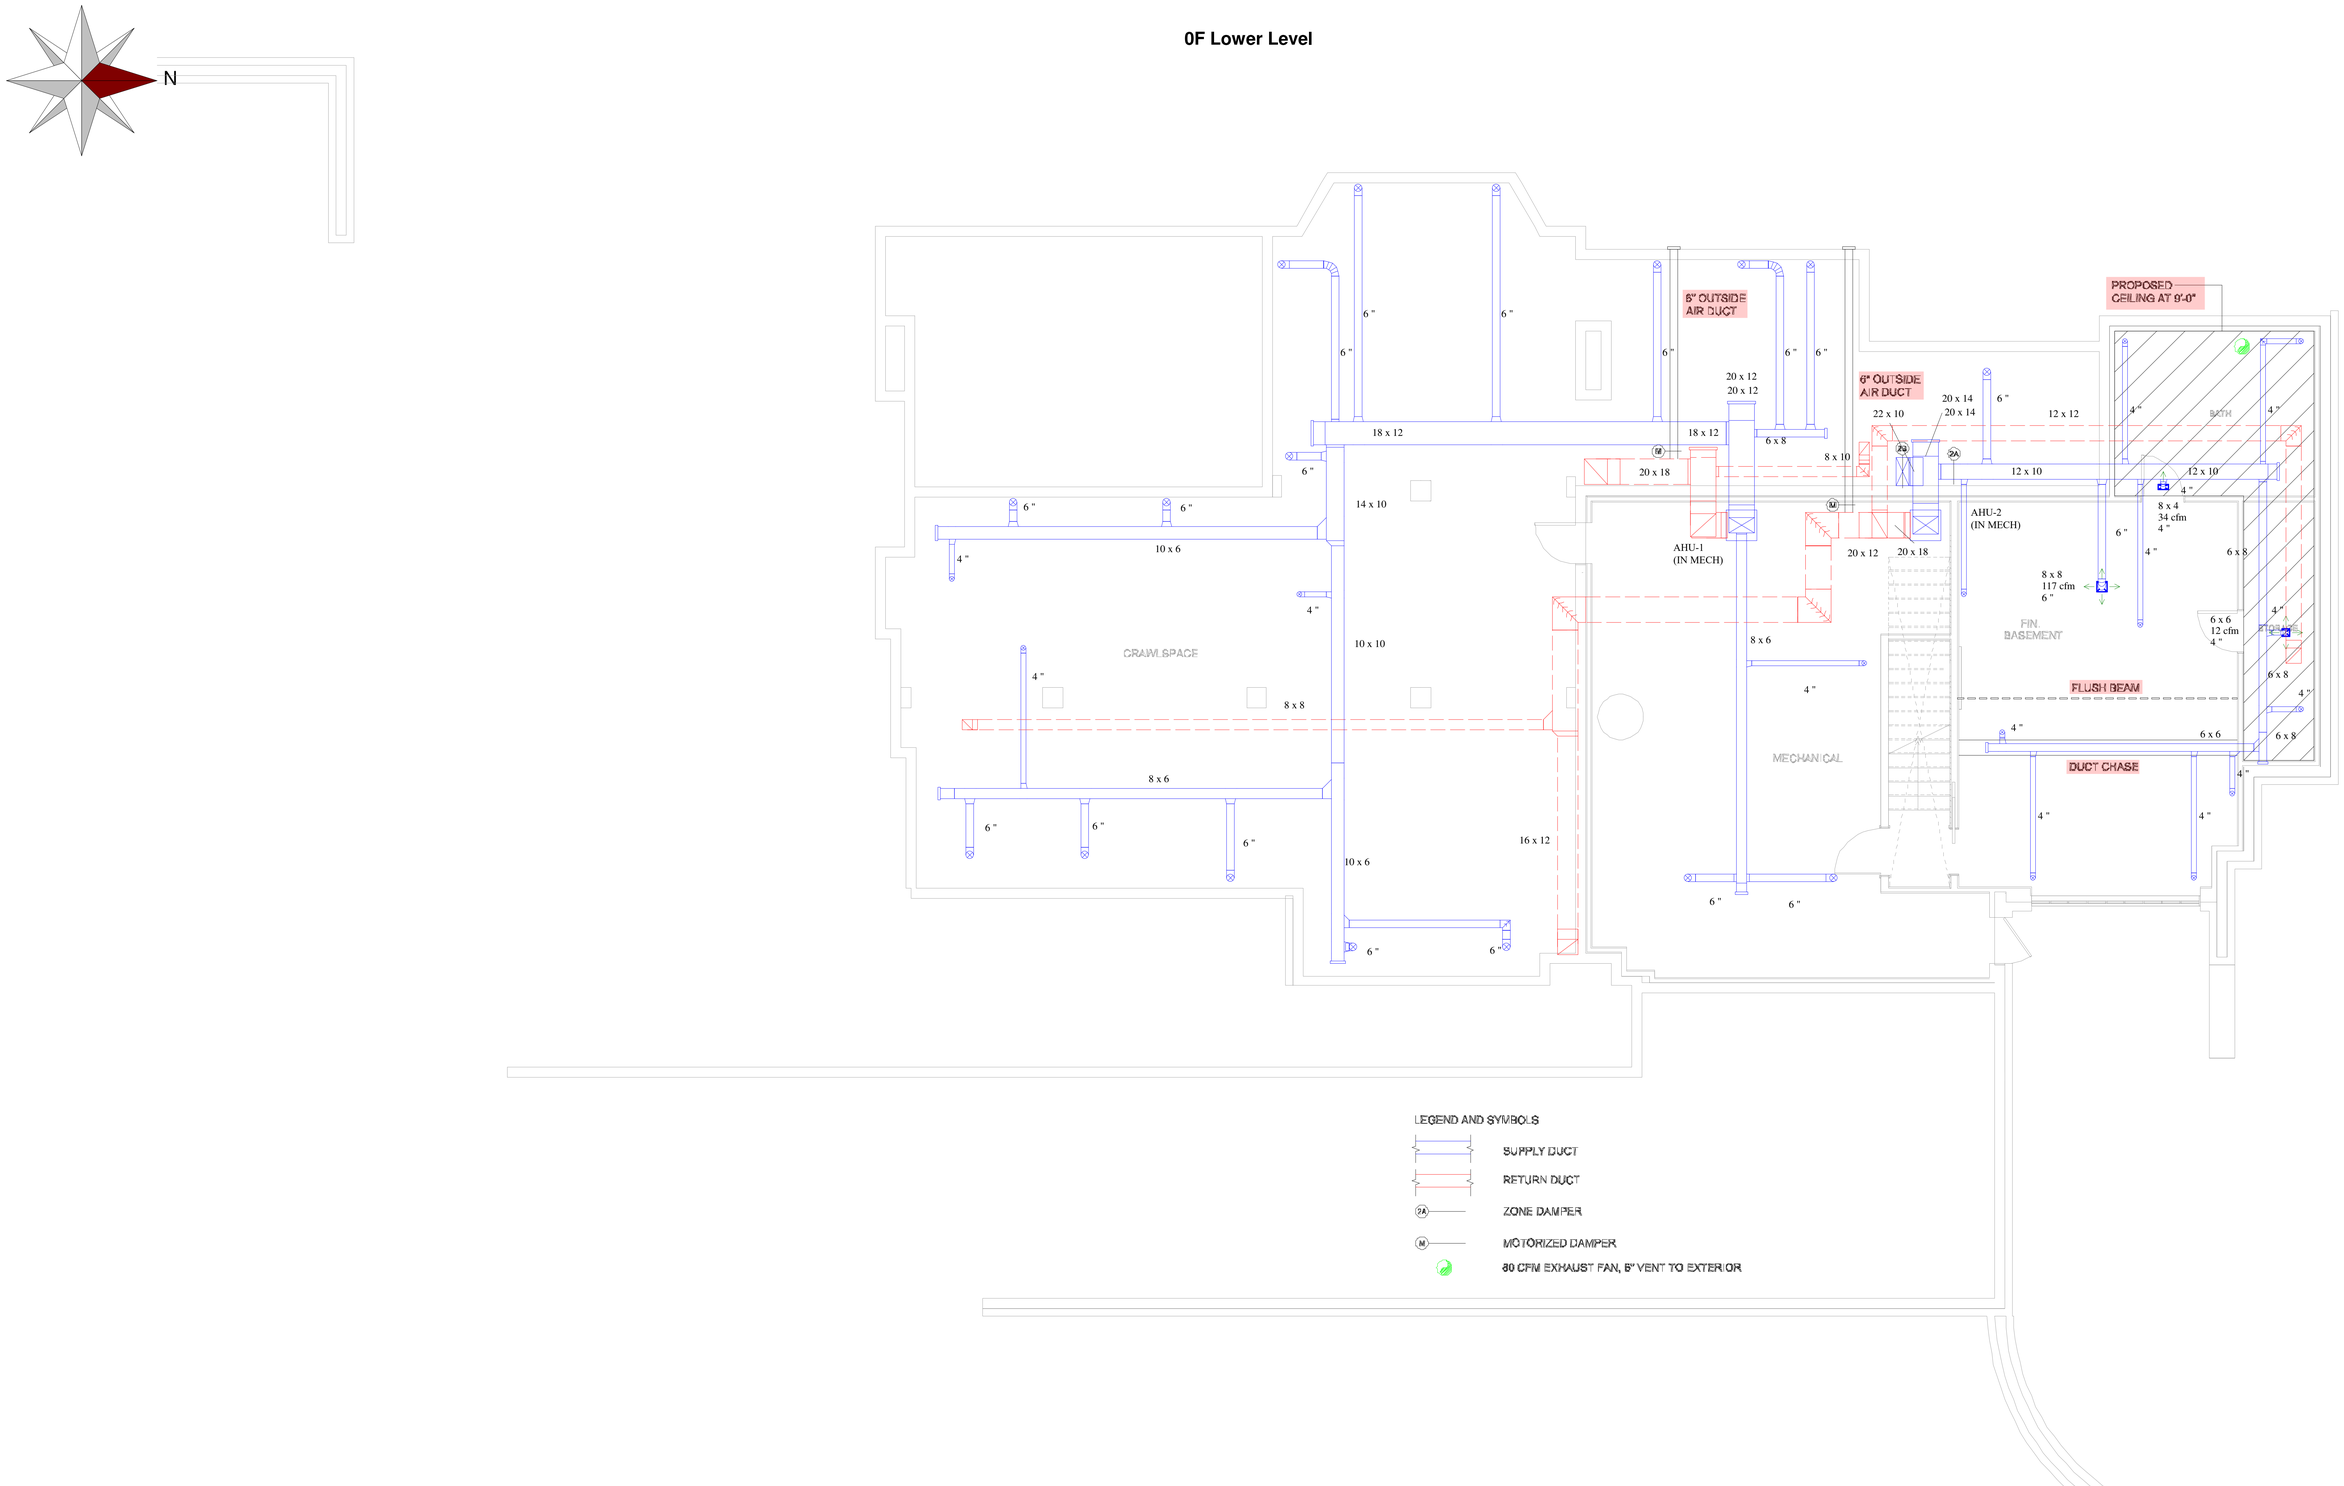

ProCalcs "We are the missing piece" CAC1821635 ProCalcs, LLC

Digitally signed by Dana Mejia
Date: 2025.08.04 10:49:25 -04'00'

APPROVED
By Richard at 9:54 am, Aug 04, 2025

REVIEWED
By: Tim Malada at 9:24 am, Aug 04, 2025

Job #: Scott Residence
Performed by Jayvee Layug for:
Scott Residence
15 Stuyvesant Rd
Biltmore Forest, NC 28803

ProCalcs, LLC
P.O. Box 882032
Port Saint Lucie, FL 34988
Phone: 772-882-5700 License: CAC1815254
www.ProCalcs.Net tom@procalcs.net

Scale: 1/4" = 1'0"
Page 1
Right-Suite® Universal 2025
25.0.03 RSU27939
2025-Aug-04 19:15:47
...ing Drawings\Scott Residence.rup

1F Main Level

Job #: Scott Residence
Performed by Jayvee Layug for:
Scott Residence
15 Stuyvesant Rd
Biltmore Forest, NC 28803

ProCalcs, LLC
P.O. Box 882032
Port Saint Lucie, FL 34988
Phone: 772-882-5700 License: CAC1815254
www.ProCalcs.Net tom@procalcs.net

Scale: 1/4" = 1'0"

Right-Suite® Universal 2025
25.0.03 RSU27939
2025-Aug-04 19:15:48
...ing Drawings\Scott Residence.rup

2F Upper Level

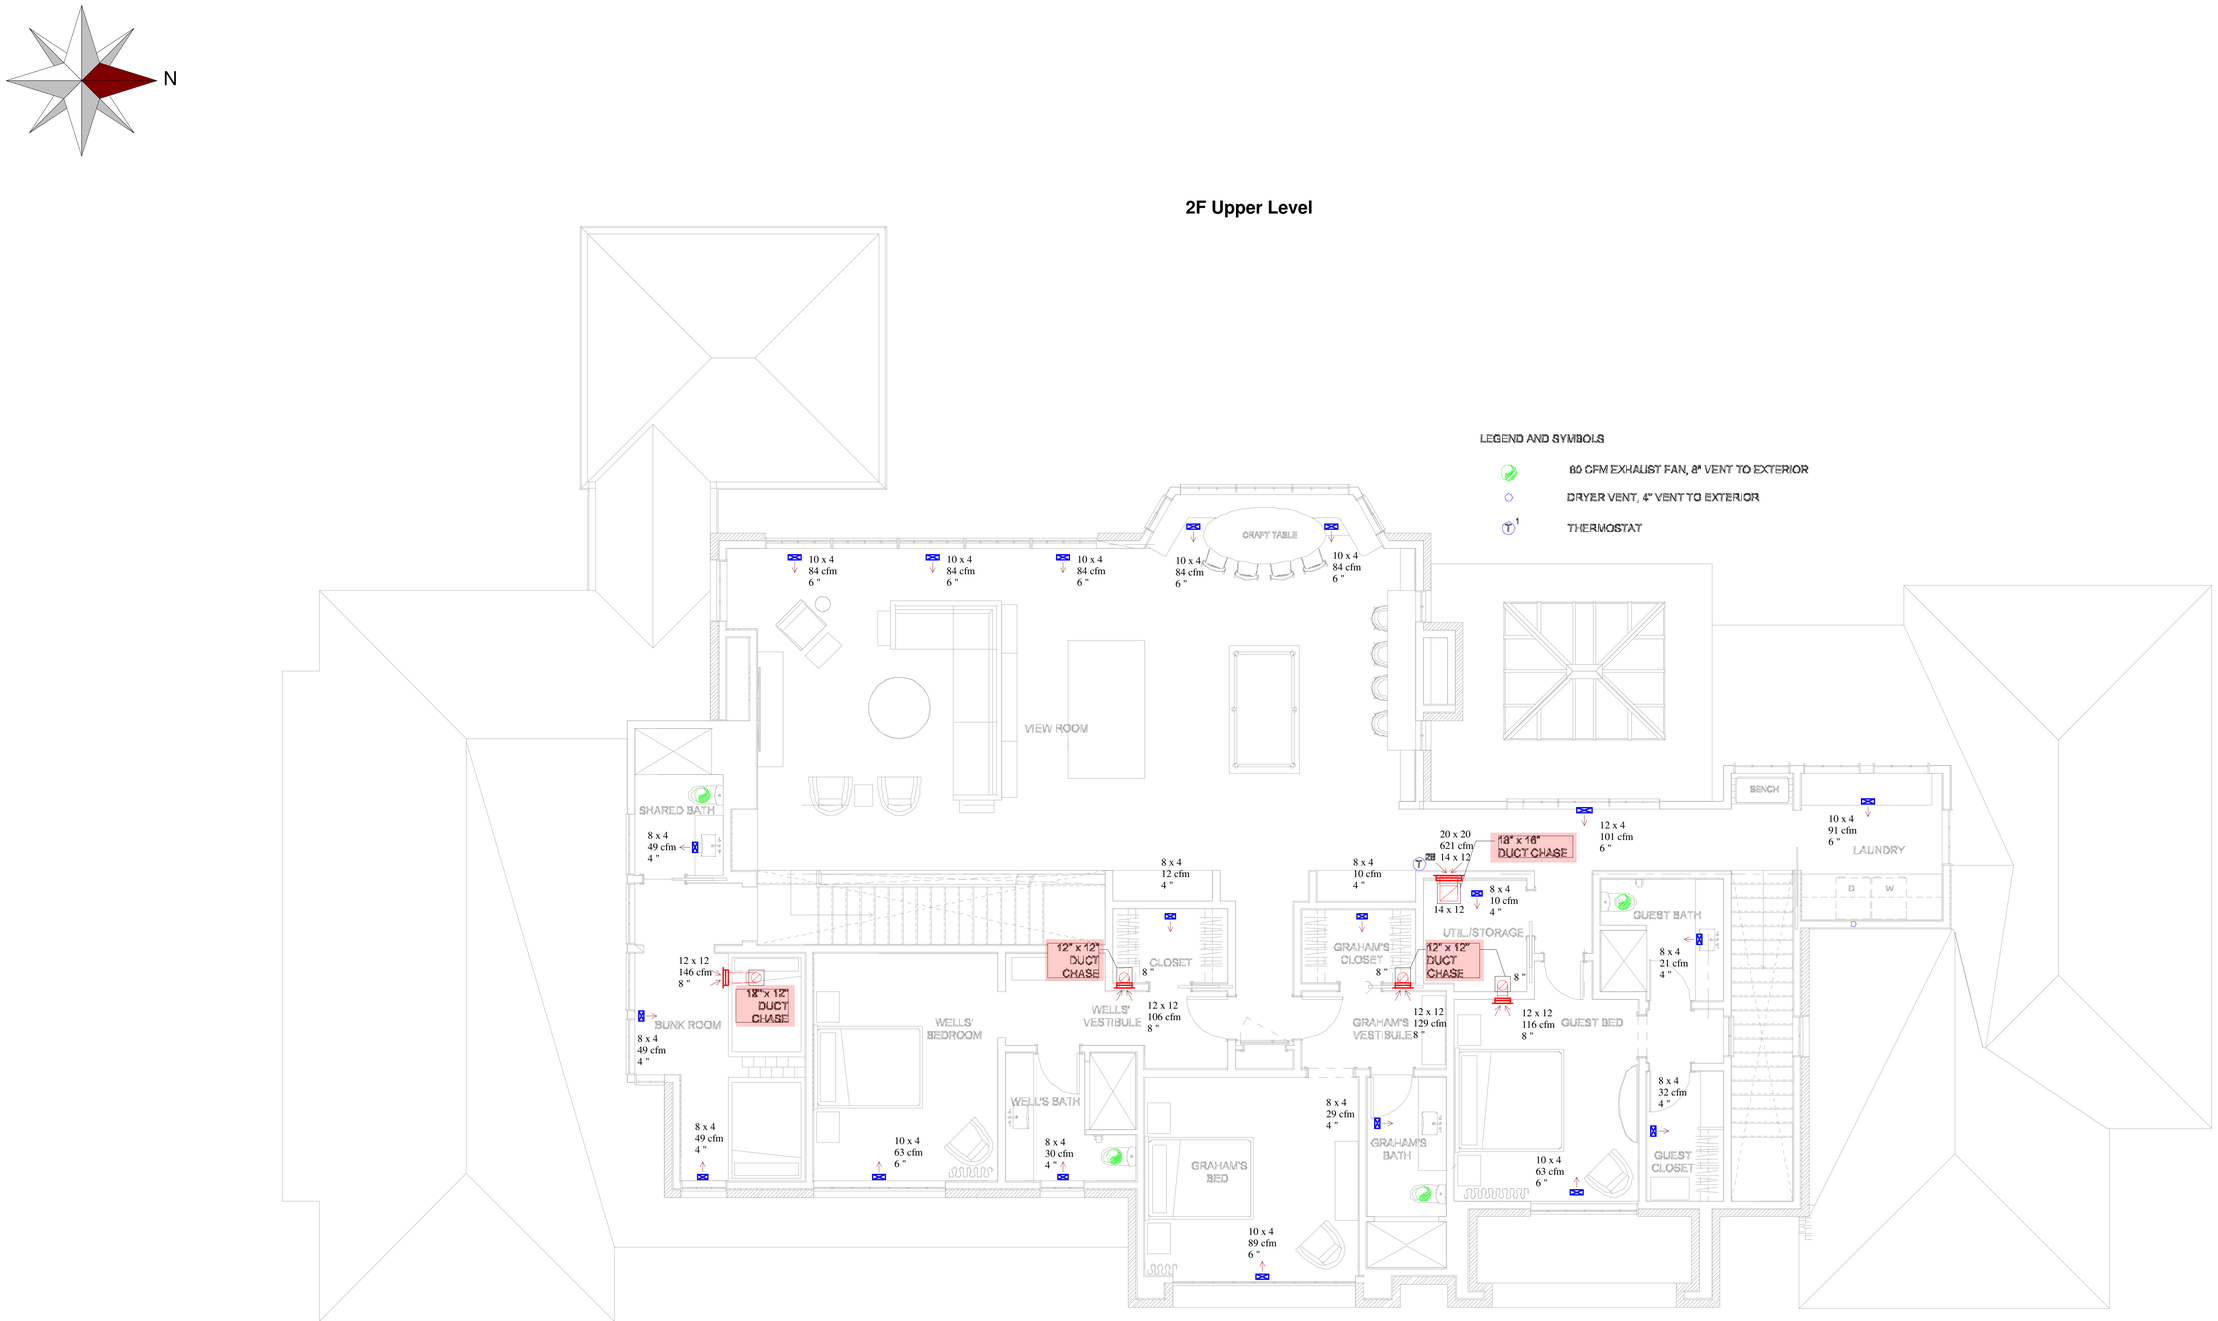

Job #: Scott Residence
Performed by Jayvee Layug for:
Scott Residence
15 Stuyvesant Rd
Biltmore Forest, NC 28803

ProCalcs, LLC
P.O. Box 882032
Port Saint Lucie, FL 34988
Phone: 772-882-5700 License: CAC1815254
www.ProCalcs.Net tom@procalcs.net

Scale: 1/4" = 1'0"
Page 3
Right-Suite® Universal 2025
25.0.03 RSU27939
2025-Aug-04 19:15:51
...ing Drawings\Scott Residence.rup